REFERENCIAS:

- Red Suc. Río de la Plata
- Lazo a Red otro esquema
- MT>1000KVA
- MT<1000KVA
- Lazo a 7 KV
- Int. S.E. de Hexafluoruro
- R4/R8: Año de instalación 1994/98
- Cámara inundable
- XC1/XC2: Capacitores 50kVA/30kVA

Por favor colocar: A (ABSE) · L (LIBRE) · ND (No Disp.) · F (Func.) · xTR (Por Transf)

ACTUALIZADO

Fecha: 21.11.13 Firma:

PASADO

Encargado Sr.Oscar 4814-5444
Pedrosa Gustavo 1550071446
Nocturno llaves Encargado edif.lindante

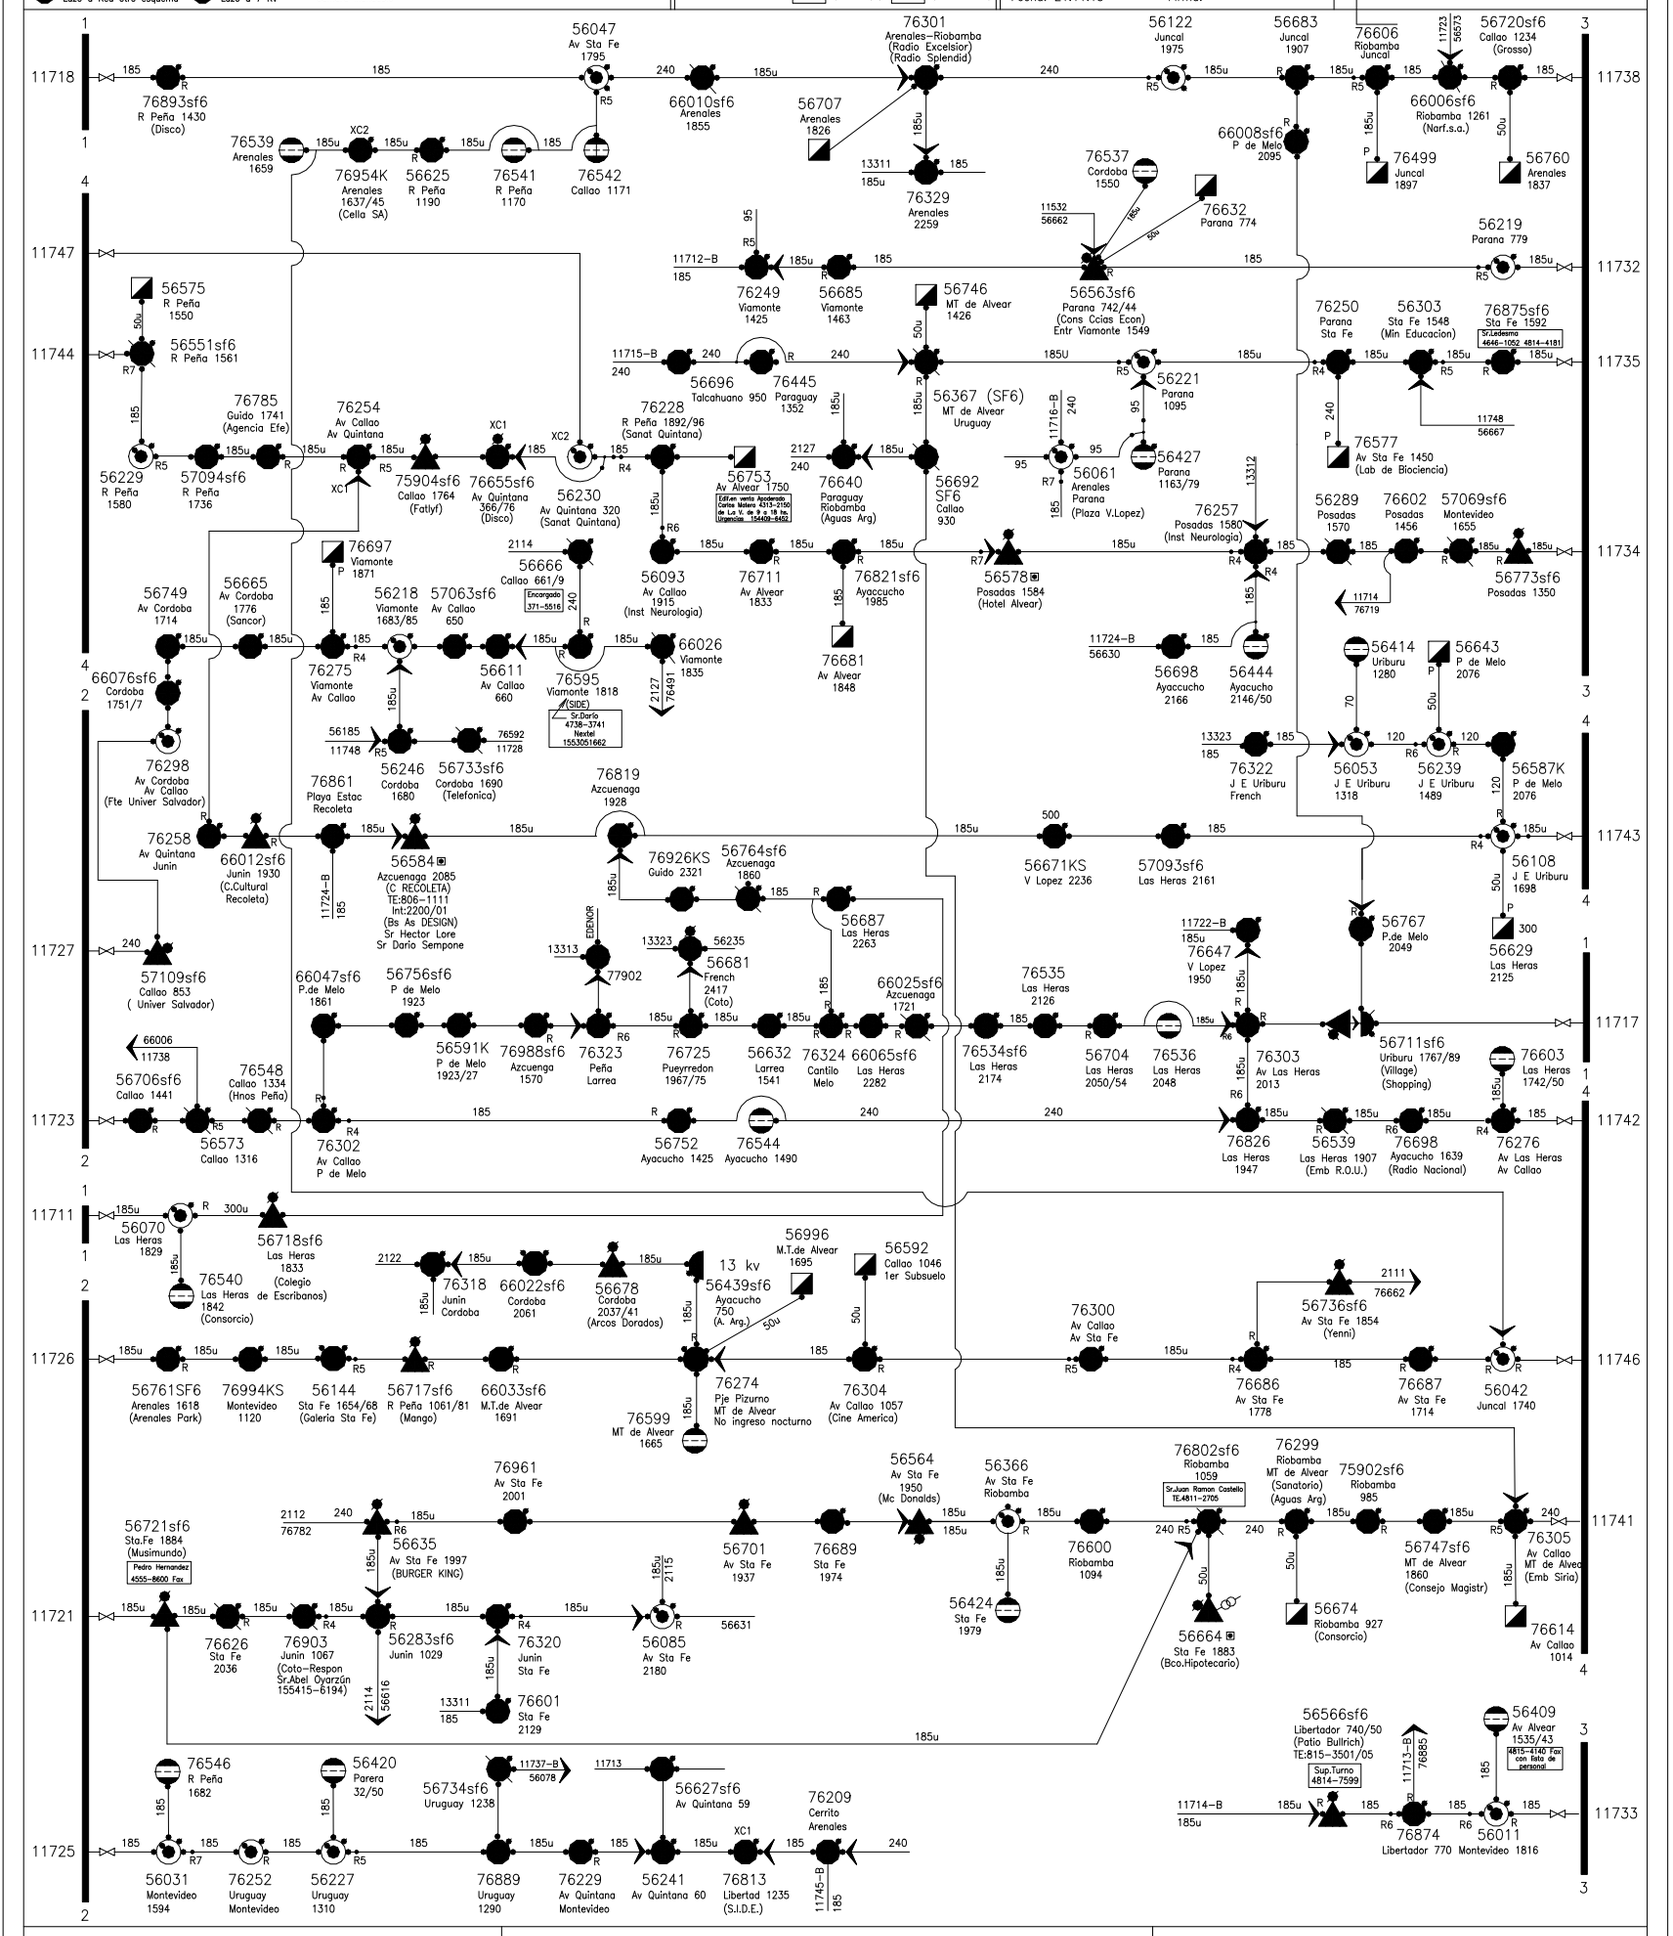

EDESUR S.A.

DEPARTAMENTO OPERACION M.T.

Sistema de Gestión de Redes

Mantenimiento del Sistema y Actualización de Esquemas y Mural

R.A.T.

B.C.
S.I.

106 80 I · 107 80 II · 300A

IV · I · II · III

PARANA A

S.E. N°117–12,9kV–Telemando

Dir.: Las Heras y V Lopez (Plaza) Tel.: 718–614