Red Suc. Gral Paz
Red Suc. Río de la Plata
Lazo a Red otro esquema
Mallado por BT
Red Edenor
Lazo a otra tensión
Int. PVA
Int. AIRE
Int. GVA
Int. SF6
Int. VACIO
Int. MAGNETICO
R4/R8: Año de inst. 1994/98
XC1/XC2: Capacitores 50kVA/30kVA
MT>1000KVA
MT<1000KVA
Llave en Zonal
Límite Explot. TI
Toma N° Inhibida
CABLE 7 kV
EA = Equipo Abierto
Cámara inundable
M I E Medidor de intercambio de energía

ACTUALIZADO	PASADO
Fecha: 04.12.13 Firma:	Fecha: Firma:

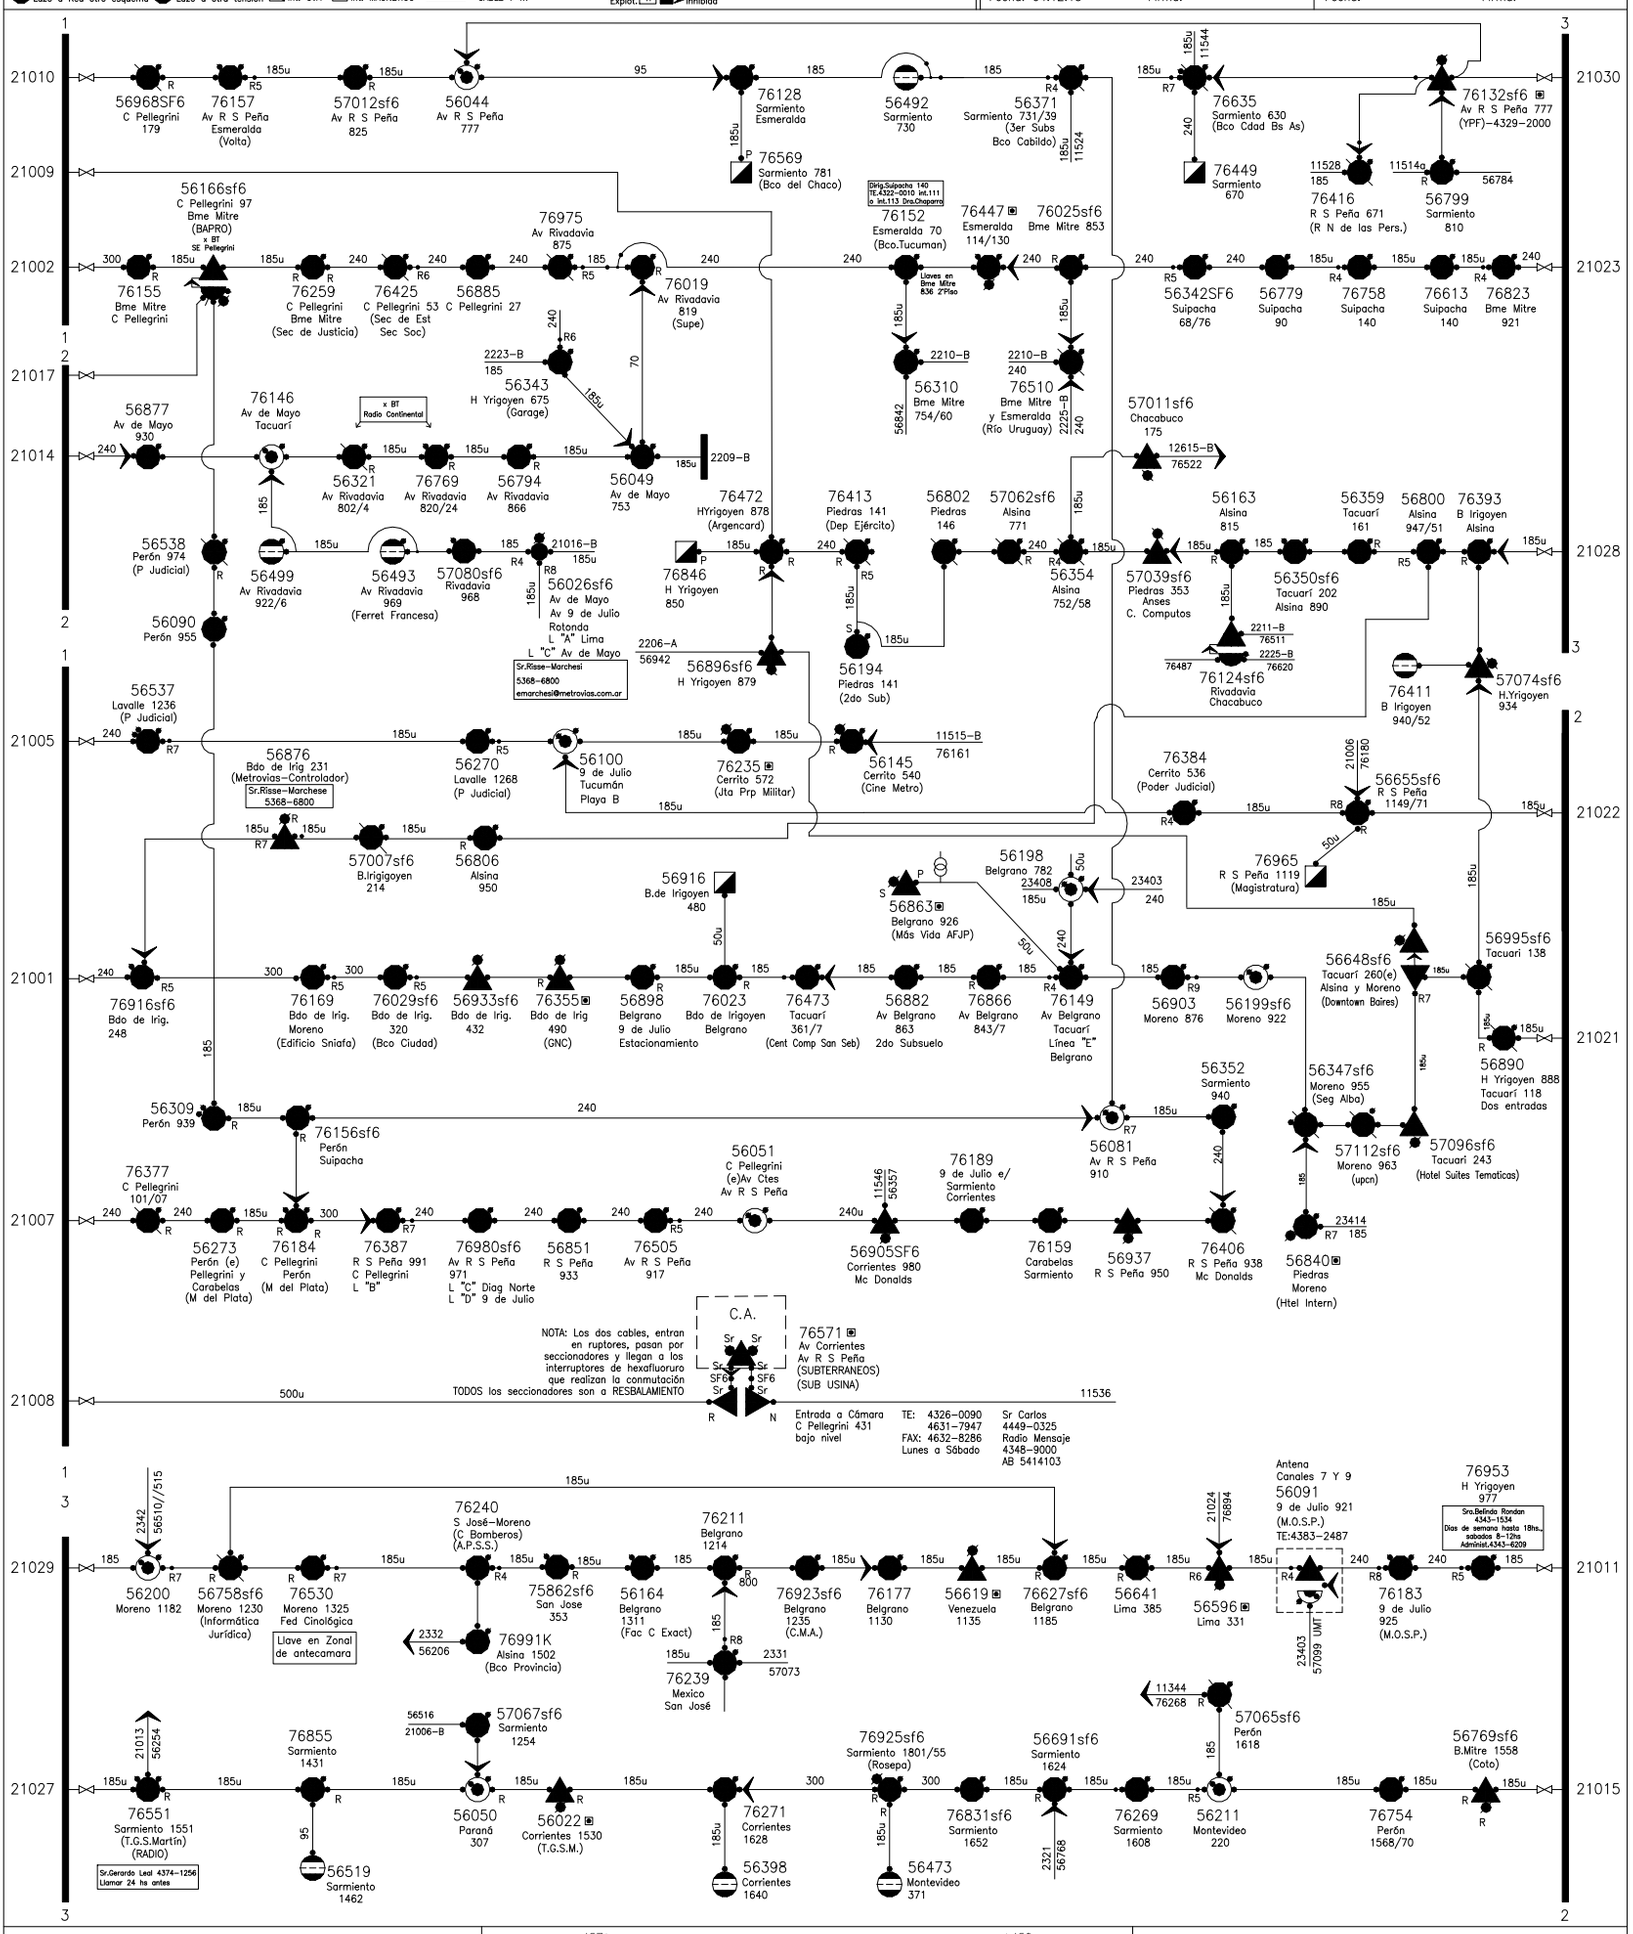

EDESUR S.A.

DEPARTAMENTO OPERACION M.T.

Sistema de Gestión de Redes

Mantenimiento del Sistema y Actualización de Esquemas y Mural

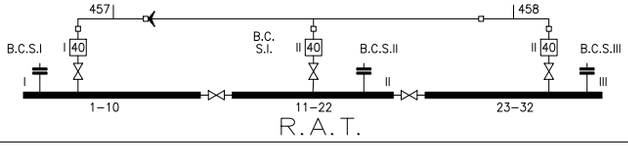

C. PELLEGRINI A

S.E. N°210-13,0kV-Telemando

Dir.: C. Pellegrini e/Riv. y B. Mitre Tel.: 718-3410 -3403